


E Building Level 1

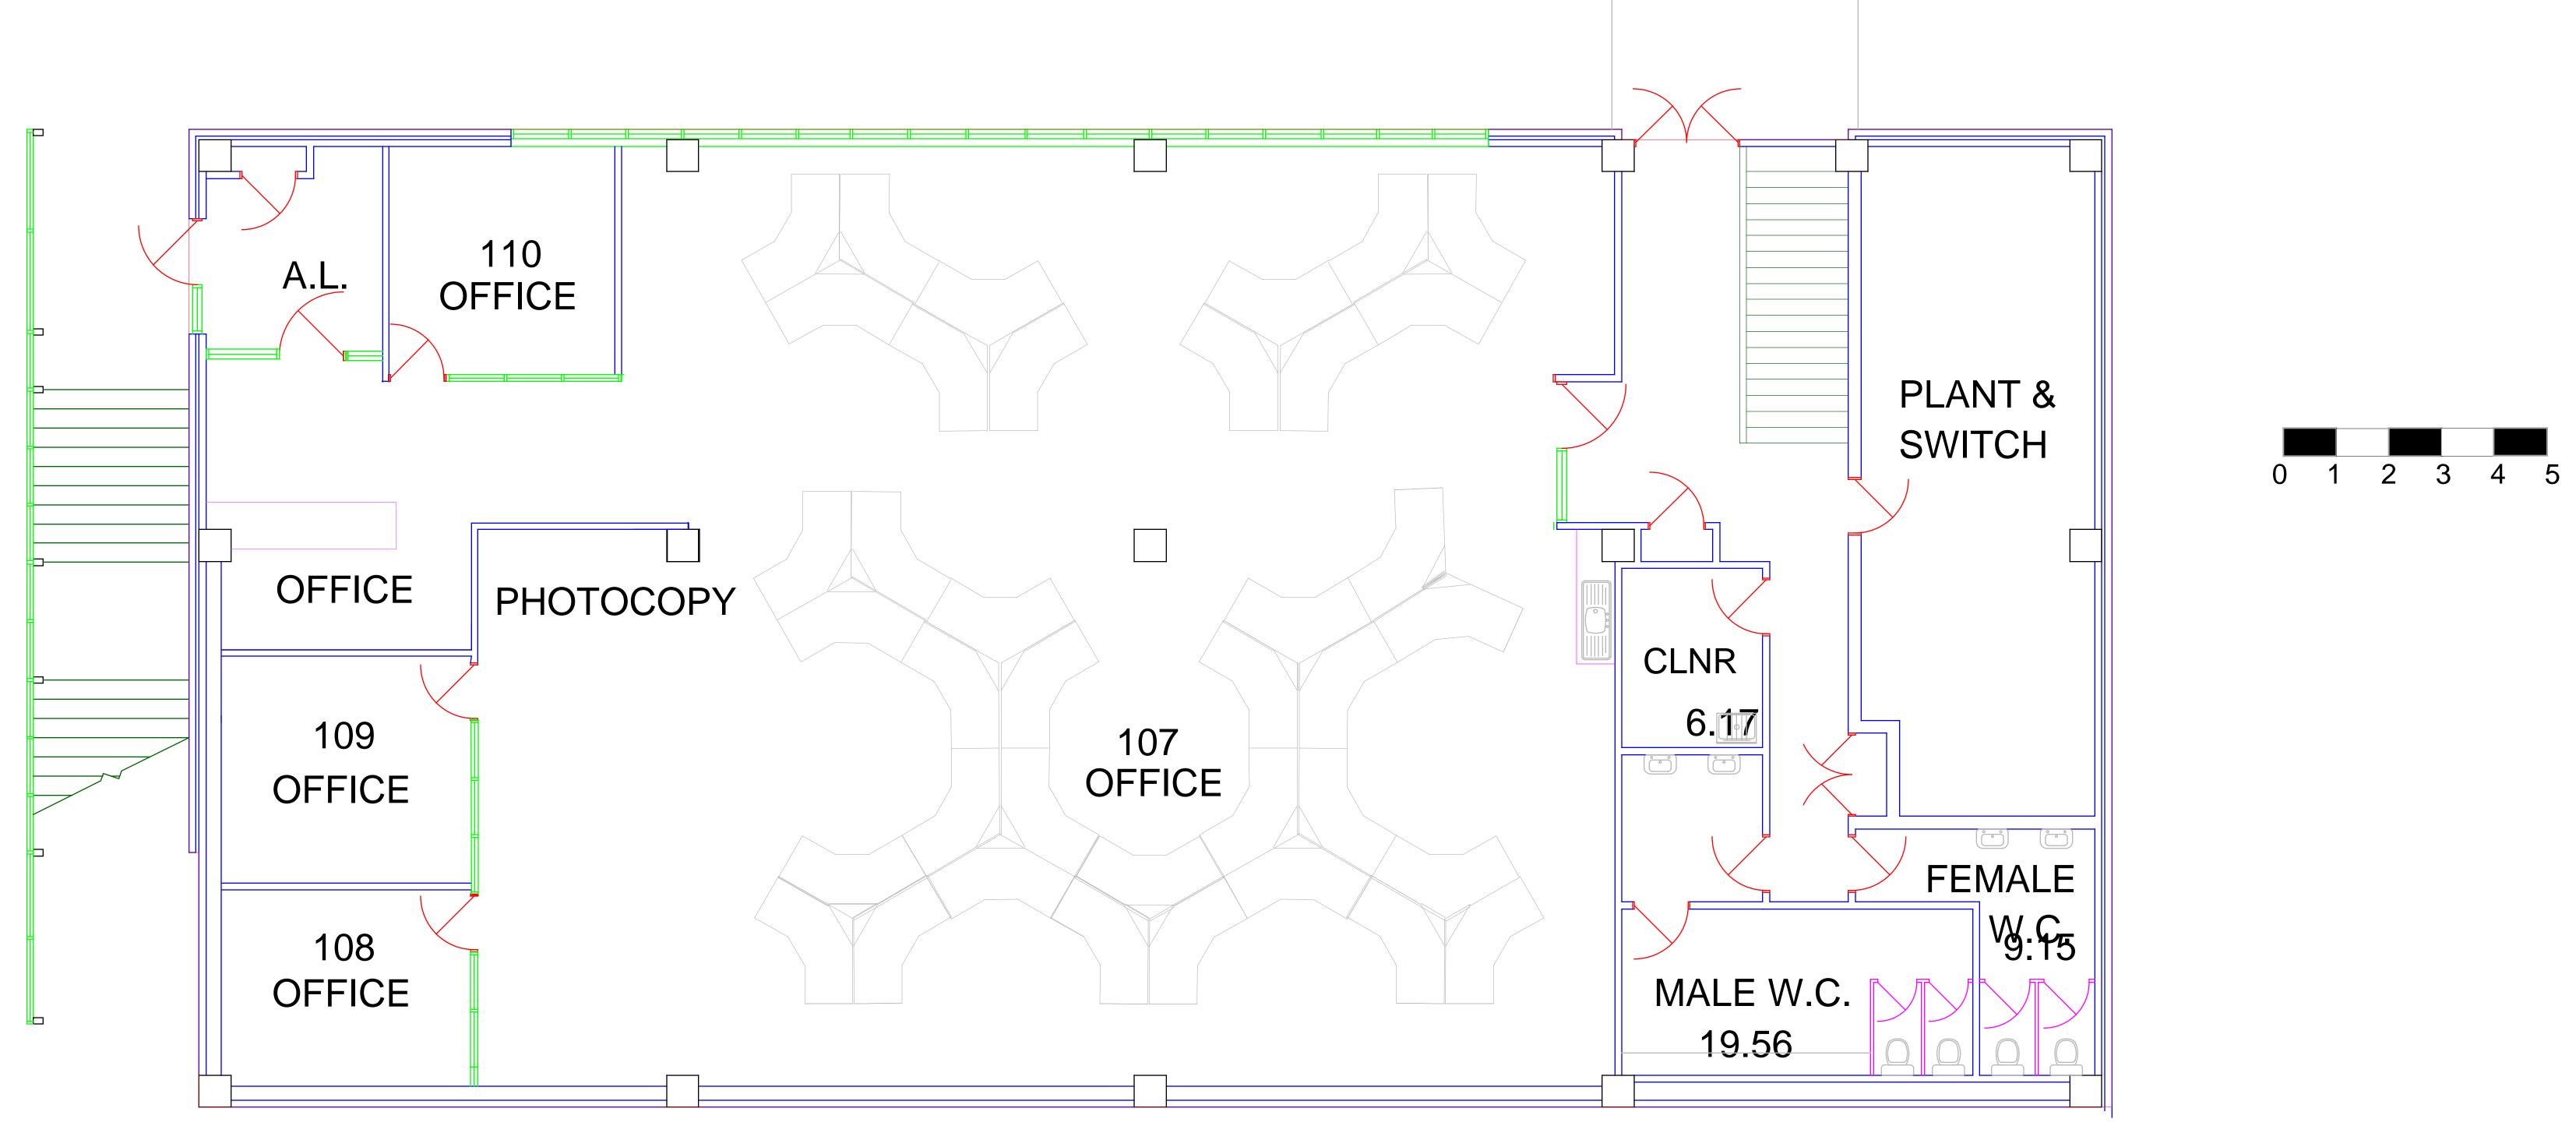

Printed: 17/12/2018